XCITY

国际总体规划与城市设计竞赛

机构赛道 · 设计任务书



本次竞赛场地约 1,656 km²
全域框架 · 一期城市设计 · 重点节点

第一轮初步构想 → 五家入围 → 第二轮完整设计
设计补偿及优胜奖金总额 US$300,000

目录

01 竞赛概况

02 设计命题

03 区域背景

04 场地

05 现状条件

06 愿景与目标

07 设计范围

08 功能与指标要求

09 约束条件

10 设计考量

11 分期与实施

12 成果要求

13 评审标准

14 规则与流程

附录 场地资料

竞赛概况

XCITY拟在阿根廷圣胡安省建设以能源和算力为基础、生产与公共生活共同发展的新城。本次面向专业设计机构及联合体，征集全域空间框架、一期总体城市设计和重点节点方案。

项目	内容
地点与范围	阿根廷圣胡安省，安第斯山前地带；本次竞赛场地约1,656 km²
先行区	固定试点：光伏农业田01–03共13.9 km²、生活区一期2.48 km²（仅外轮廓）；由XCITY自建，方案须衔接，不得改画
参赛方式	免费公开申请。所有申请人适用统一申请要求、资格审核与评审标准
第一轮	官网注册后，通过邮件专属链接在线填写、上传并最终提交完整申请及1–10页构想PDF；先审资格，再结合构想、团队与业绩选出五家
第二轮	5家入围机构签约并收到完整任务书、资料包后开展完整设计；通过线上介绍与统一答疑了解场地
费用	每家第二轮有效提交机构补偿US$50,000；1家优胜者额外获US$50,000，总额US$300,000
后续服务	深化设计另行洽谈，服务范围、费用及成果使用权另行签约

设计命题

XCITY希望在阿根廷圣胡安省，将能源、算力、农业与相关产业组织为新城的经济基础。本次设计需要说明，这些生产活动如何支撑就业、长期居住、公共服务与日常生活，并在真实场地条件下逐步形成城市。

核心命题

这块土地应当怎样发展成一座人愿意生活的城市？
一期从哪里开始，如何在资源约束下形成完整的生产与生活关系？

01 生产如何支撑城市

说明谁在这里工作和生活，产业怎样产生岗位与服务需求。将人口、住房、公共服务与能源、算力和农业的实际规模相互校核。

02 场地如何决定布局

水资源、地形、季节沟道、强日照与风沙应实质影响选址、密度、道路和开放空间。解释哪些地方应建设、生产或保留。

03 一期如何成立

提出能够独立运行的一期，落实必要道路、水电、生产运维、住房和公共服务；说明后续暂缓时的运行方式和继续扩展的条件。

AI智能体、机器人和自动驾驶带来的变化，应落实到岗位、服务、街道与空间使用中，并由街区和节点设计加以验证。

区域背景

人口

圣胡安省2022年人口普查为822,853人，较2010年增长约20%，主要集中在大圣胡安地区。

矿业

2024年矿产出口14.67亿美元，占全省出口81.2%；金矿及新兴铜矿项目是区域经济背景。

农业

2024年圣胡安省葡萄园占全国19.8%，是阿根廷第二大葡萄种植省；开心果、橄榄及加工也与本项目相关。

能源

源资料记录截至2024年底有21座运营光伏电站、装机547.4 MW；当年光伏满足约54%的省内用电需求。

水资源

灌溉农业依赖圣胡安河及Los Caracoles、Punta Negra、Ullum等水库。干旱和供水变化是规划的重要条件。

连接与地震

RN 150经高海拔Agua Negra山口通向智利。季节性通行不能与未来隧道设想混同；地震历史要求重视应急交通和韧性。

区域背景沿用源资料标明年份的数据；省域总量不等于项目已取得的水权、并网能力或需求。

区位



南美洲 · 圣胡安省




圣胡安省及周边区域

场地位于阿根廷西部圣胡安省、圣胡安市东北方向。区域联系涉及省会及周边聚居地、农业和矿业服务网络，以及面向阿根廷内陆和智利的交通。

设计应说明首期与既有城市的服务分工、就业采购和交通联系。区域研究可以超出项目边界，但不形成边界外的开发权利。


底图：Natural Earth；省界：amCharts geodata；场地范围：XCITY提供资料。本图用于区域关系示意。

区位与交通

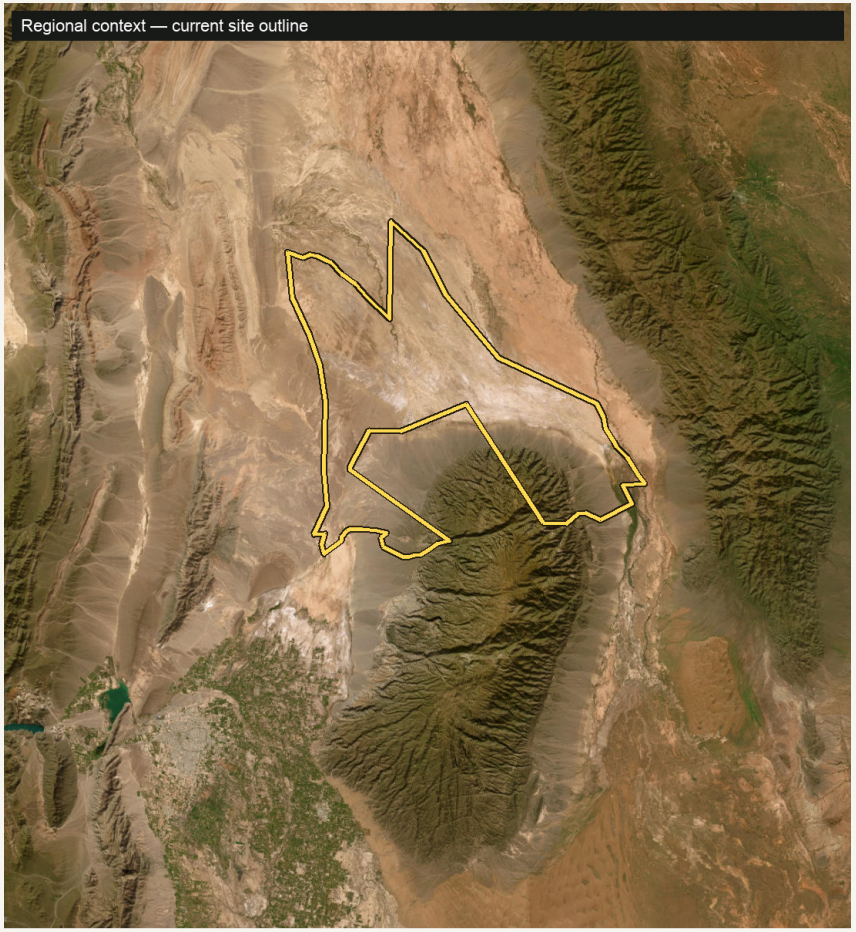

Source: Esri, Vantor, Earthstar Geographics, and the GIS User Community
Accessed 2026-10-27 | multi-date mosaic, not a site survey
Boundary: 2026-10-27-open-seam-closure

真实卫星拼接影像：Esri World Imagery；署名见图内。访问：2026-10-27；不同位置拍摄日期不同，非同期现场测绘。黄色线直接采用本次开放接缝闭合后的同源边界。

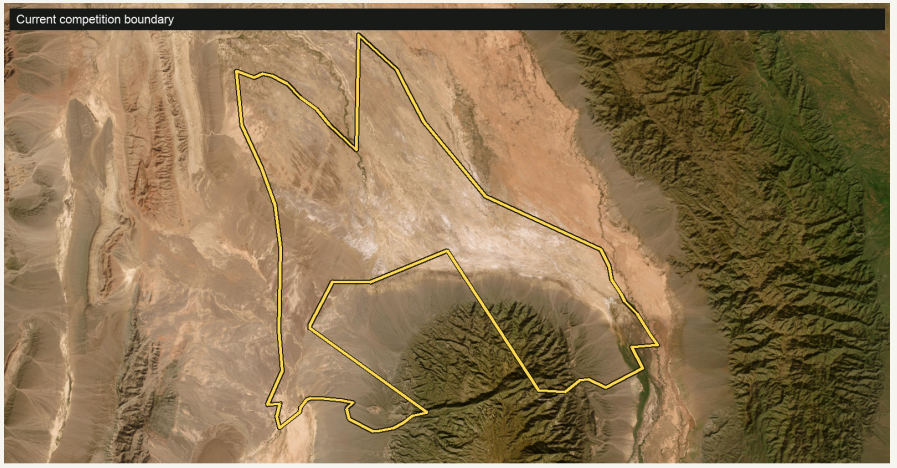


Source: Esri, Vantor, Earthstar Geographics, and the GIS User Community
Accessed 2026-10-27 | multi-date mosaic, not a site survey
Boundary: 2026-10-27-open-seam-closure

RN 40	南北向区域干线	27.6 km
RN 20	省会及东部方向	40.7 km
RN 141	东向区域联系	47.3 km
RN 150	智利方向区域联系	52.9 km
RP 510	东侧省道	35.6 km

距离为本轮场地边缘至现有道路的最近直线距离，并非实际行驶距离。各方向进场道路的路由、权属及工程量由方案论证。

先行区

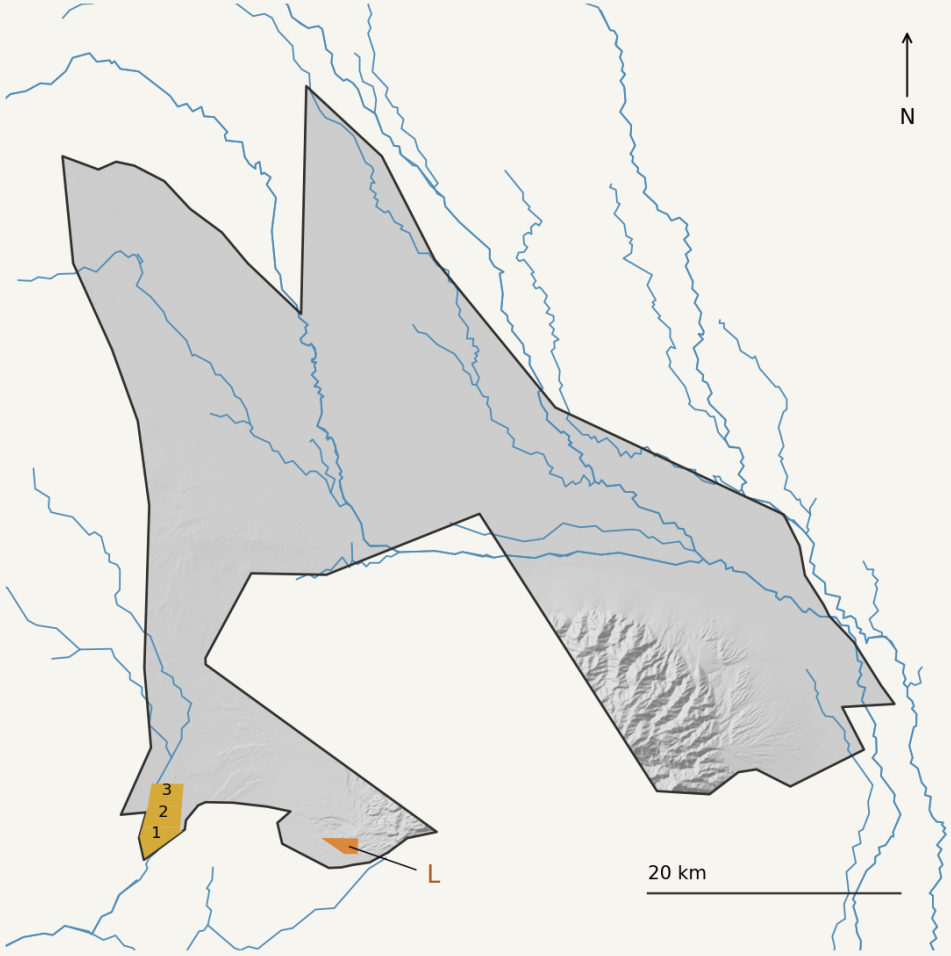

固定试点区

光伏农业田13.9 km²


生活区一期2.48 km²

两处试点均由XCITY自行建设，范围及内部布局不得改画或新增建筑。须说明街道、供水、能源和服务衔接。图中01–03为光伏农业田，L为生活区一期外轮廓。

一期选址应比较与先行设施衔接的条件。不能只把先行区作为远景图中的背景，也不能据图示推定全部设施已经运行。

气候

区域气候干旱、降水稀少、温差明显。高温、强日照、风沙和Zonda风应进入街道朝向、遮阴、设备进风、清洁用水与公共空间的设计判断。

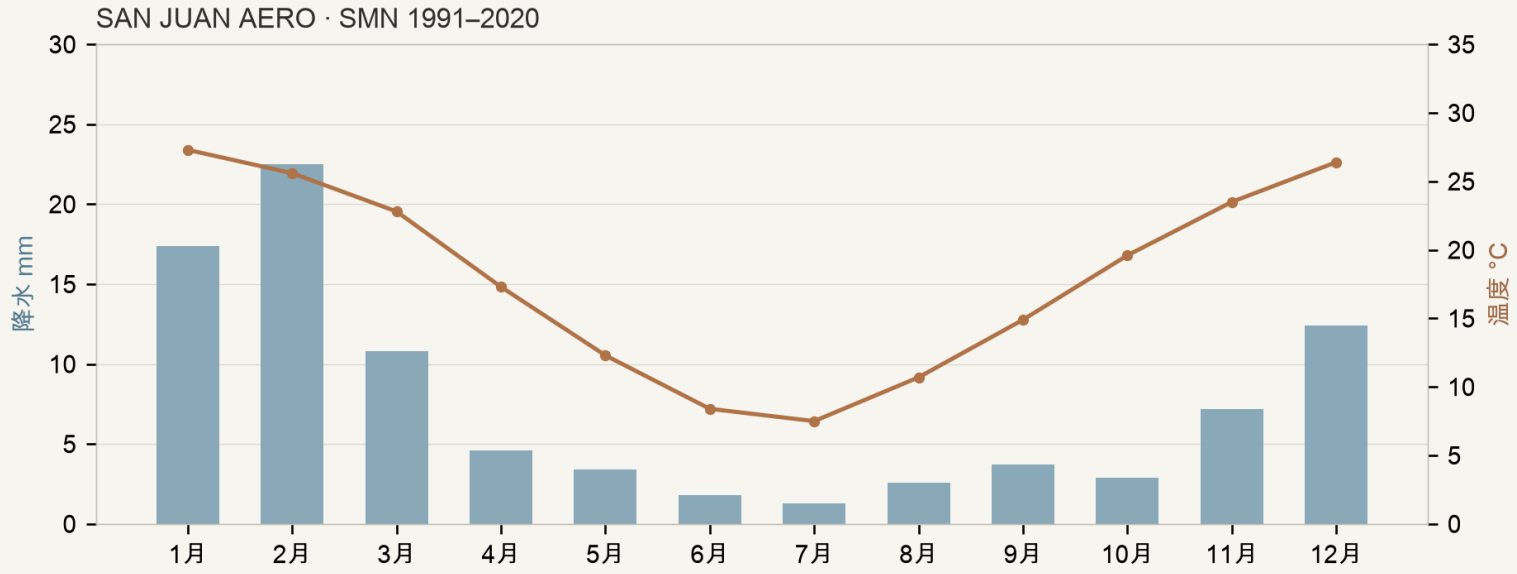


90.5 mm
年降水量

18.0 °C
年平均气温

27.3 / 7.5 °C
1月 / 7月平均气温

来源：阿根廷国家气象局SMN，SAN JUAN AERO站，1991–2020气候标准值；海拔597 m。图中为月平均温度，不是月平均最高温。机场站仅作区域参考，场地海拔与局地条件须另作判断。

地形与坡度

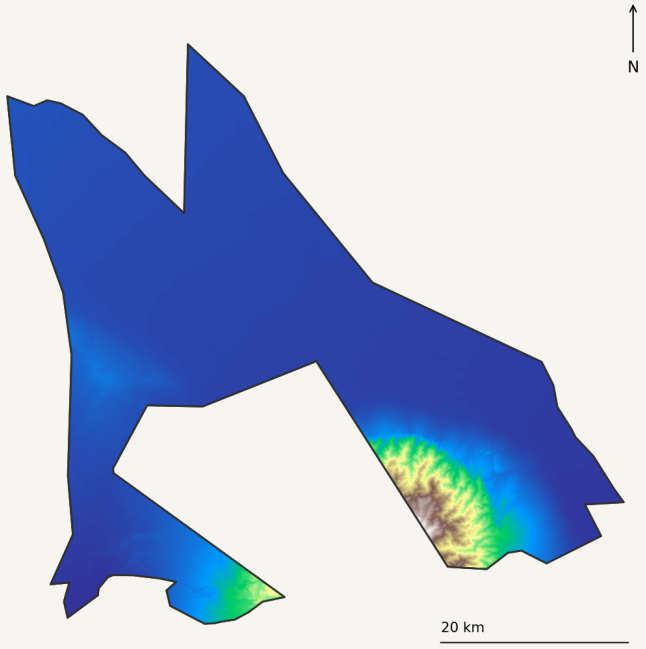

高程 · 约636–1,354 m（5%–95%分位）

最高点约2,658 m；DEM最低点约606 m



坡度分级 · 本轮范围重新计算

- <2% 约1,183.6 km²
- 2–5% 约182 km²
- 5–15% 约132 km²
- >15% 约158 km²

仅修复9/13地块接合处获授权的开放狭缝，其他外边保留；几何面积1,658.819819 km²（2026-10-27-open-seam-closure），项目名义面积仍约1,656 km²，不替代地籍核实。地形采用Copernicus GLO-30 DEM，60 m网格、300 m坡度平滑；栅格面积为近似值。

水文与可建设用地

季节性沟道



沟道按DEM上游汇水面积分级。用于识别汇水与空间连续关系；不等同于常年有水的河流。

洪泛敏感性筛查



敏感筛查约503 km²：距汇水≥100 km²沟道1.5 km内、相对沟底高度<3 m的初步筛查。


初步适建条件筛查



坡度<2%且在现行敏感筛查之外的用地约686 km²。筛查不等于建设许可，也不自动排除其他土地的设计可能。

现行资料包方法：60 m DEM、D8汇流及HAND；分析域外上游汇水未计入。约503 km²为敏感筛查，不是实测洪水边界或整体禁建区；新封闭接缝尚未纳入此既有洪泛模型分类。须结合水权、地质、生态、权属及专项勘察判断；干河床内不得布置永久建筑。

五大城市系统

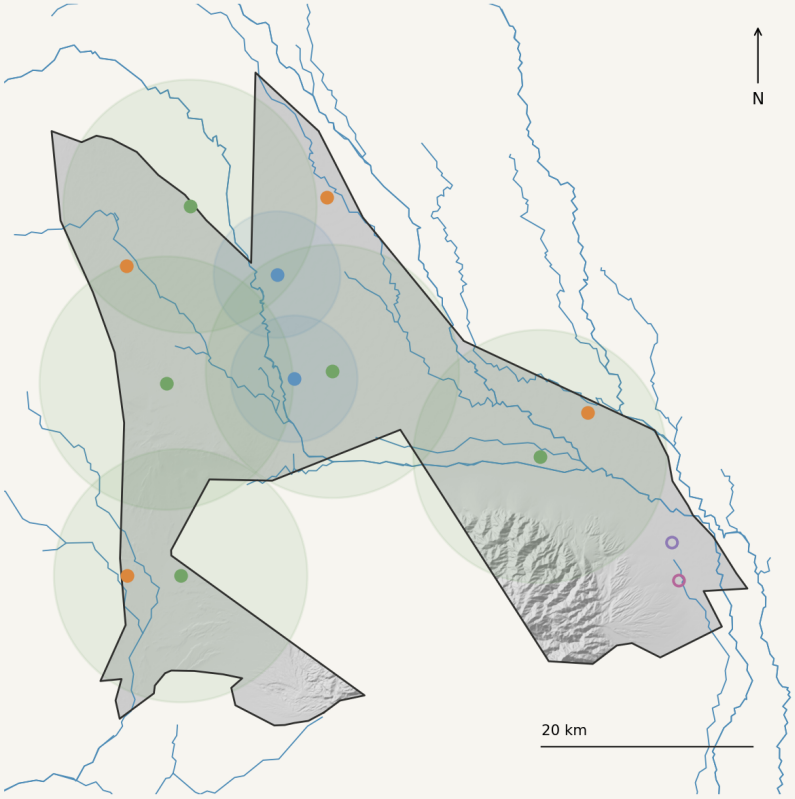

能源与算力

接近可靠供能、通信和维护通道；比较冷却与取水条件、洪水安全及住区缓冲。

农业生产

保留农光生产系统，组织外围作物、灌溉、加工与仓储；按资源条件确定规模。

居住与公共生活

群居聚落承载公服与街道生活；庄园围绕私人土地，须说明土地消耗、服务及交通成本。

产业与自动化

聚落型加工、制造、维修和场内物流随各期配置；门户型生产依赖对外通道与资源条件。


对外贸易与门户

研究货运、仓储、转运及未来贸易接口；口岸、保税等性质须以相应批准条件为依据。

采用现行资料包中的系统意向，非固定选址或用地边界。方案可保留、移动或调整，并说明依据；圈示不代表用地面积。


五大城市系统 · 分项示意

能源与算力

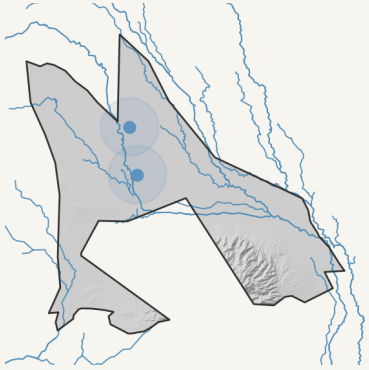


接近可靠供能、通信和维护通道；比较冷却与取水条件、洪水安全及住区缓冲。

农业生产

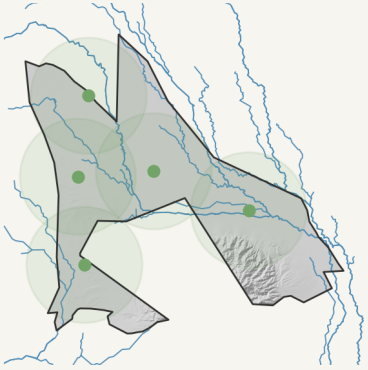


保留农光生产系统，组织外围作物、灌溉、加工与仓储；按资源条件确定规模。

居住与公共生活

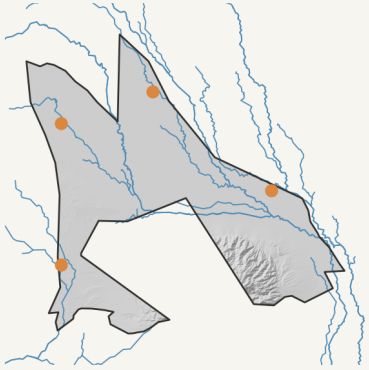


群居聚落承载公服与街道生活；庄园围绕私人土地，须说明土地消耗、服务及交通成本。

产业与自动化

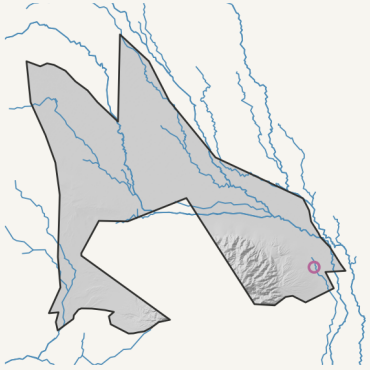

聚落型加工、制造、维修和场内物流随各期配置；门户型生产依赖对外通道与资源条件。

对外贸易与门户

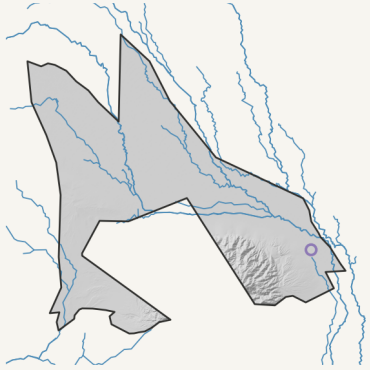

研究货运、仓储、转运及未来贸易接口；口岸、保税等性质须以相应批准条件为依据。

实心点为现行资料包的系统意向，空心点为预留功能；圈示不代表用地边界。门户功能须论证位置、接入与阶段，示意不预先分配五大系统用地比例。

已确定的系统构成


原项目提出光伏农业与模块化算力设施的系统组合。机构应保留系统逻辑，检验其空间、资源和运维接口；下列图片是原项目意向与产品参考，不是现场照片。





光伏农业 · 板下与外围

霍霍巴、迷迭香、饲用仙人掌、羊驼与补饲设施构成原稿的共生组合。高株及藤本作物与板阵分开组织。校核成株净高、组件受光、通道、动物与设备保护；具体农艺性能须有依据。

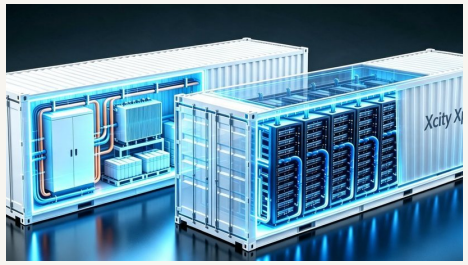



算力 · POD模块与集群

沿用XCITY POD的模块化、工厂集成和分布式部署思路，落实电、水、光纤、运输、维护消防和缓冲。设备负荷、冷却方式及扩容不能脱离资源条件，余热须有实际接收功能。

光伏发电 → 种植与饲料 → 放牧与加工 → 堆肥与回田

愿景与目标

以能源和算力为经济基础，结合农业生产，探索人、AI智能体与机器人共同运行的城市。新技术需要落实为就业、居住、服务和公共生活，而非孤立的设备或展示建筑。

目标	方案应证明的内容
资源与容量	以可靠水源、能源和实际产业条件推导人口、岗位、住房及负荷，区分开城、一期建成和远期
用地复合	光伏、农业、设备与城市合理复合，避免土地和资源指标重复计算
完整公共生活	形成学校、医疗、日常商业、交往和休闲的服务网络，说明不同居民及运营人员需求
分期可运行	首先建成部分能够运行，后续暂缓时仍具备必要生产生活条件；列明外部依赖
人与机器	让自动化与人的安全、可达、公共责任和空间体验共同成立

一期统一参考情景：5万人、2万岗位、200 MW算力、1–3 GW光伏。水源尚未落实，须说明供水假设；远期容量由方案论证。

设计范围与深度

层次	范围与深度	成果及表达
全域战略研究	约1,656 km²完整竞赛场地；结构性规划，区域联系可延伸至范围外	定位与容量、五大系统、生态与水、交通、能源通信及分期；建议1:50,000–1:100,000
一期总体城市设计	位置与范围由方案划定，不预设重点区面积；形成完整、可运行的一期布局	总平面、土地功能、主次路网、公服开放空间、市政接口、强度高度与实施；建议1:10,000–1:5,000
城市设计放大	自选完整或相互关联地区，说明选区理由、范围及系统关系	落实街区地块、建筑体量、公共界面、服务流线及关键剖面；用尺寸与指标验证一期布局
重点节点与策略	回应下页各项议题，按空间与系统作用组织节点，不以孤立地标替代城市	表达平面、剖面、运行和设施关系；重点局部建议1:1,000–1:500，关键断面可放大

比例尺服务于图幅与表达。所有图纸须标明范围、北向、比例尺、图例与关键尺寸；本轮达到概念规划和城市设计深度，不含报批、勘察、工程初步设计或施工图。

重点节点

六项重点空间议题自选三项深化，其余三项与五项策略议题均作策略回应，即三项深化、八项策略。每项须在总体布局及分期中落位；有关联的议题可以合并表达。

六项重点空间议题 · 选三项深化

01 城市入口与到达序列

02 居住社区与住宅原型

03 山前静域：与地形共生的休憩空间

04 物流枢纽与未来贸易接口

05 算力中心与余热利用

06 人与自动驾驶交通共享的街道

局部总平面与功能组织；建筑、景观和设施接口；交通与服务流线；关键剖面、街道断面及主要空间原型。代表性视图用于解释空间，不要求每项配置相同数量的效果图。

五项策略议题 · 全部回应

01 无人机起降与停靠系统

02 光伏农业与城市边缘

03 季节性河道与公园系统

04 艺术与文化场所

05 高温、强日照和风沙下的公共空间

说明在总体规划中的位置、空间原则、服务对象与阶段。可通过总平面、轴测、剖面、流程或系统图表达。

功能与指标要求

方案须安排下列功能，并根据推荐人口、产业和资源情景提出指标。每项数量注明范围、阶段、单位、来源及估算方法。

功能	内容	指标要求
居住与公服	住宅类型、教育医疗、商业文化及行政	人口、住房、用地楼面、公服容量与配置依据
算力设施	模块集群、冷却、缓冲与余热	分期负荷、供电、冷却方式和需水、接收功能
能源	光伏、储能、变配电和保障设施	装机及供能量、储能、夜间冬季保障与中断应对
农业生产	农光、外围种植、加工及仓储	用地、复合面积、作物、灌溉、生产服务
产业与物流	聚落型生产及场内物流；门户型功能预留	岗位、土地、货运与服务流线、接入及触发
交通	区域接入、道路、公共交通和慢行	等级、关键尺寸、可达性、服务及人机接口
市政	水源处理、污水回用、通信及废物	分项能力、服务范围、前置条件及扩容顺序

约束条件

约束	要求
干河床与洪水	干河床内不布置永久建筑。敏感性筛查用于比较选址，不作为正式防洪边界；跨越和活动设施须有安全退出与恢复策略
先行区	光伏农业田01–03及生活区一期外轮廓均固定，不得改画或新增建筑；说明街道、供水和服务衔接
坡度与山体	保护汇水与生态连续性；山前低密度建设须说明等高线、硬化、径流、道路和疏散，不能仅凭坡度判定可建
用地边界	使用同版业主提供的竞赛边界；图示连接不增加土地或构成地籍权属依据
水资源	供水、水权、需水与回用分别列明；未落实条件作为假设，说明影响及验证事项
抗震与照明	以当地适用抗震要求为后续依据，布局考虑应急及恢复；控制眩光、向上逸散和夜间设备照明

专题设计要求

1 · 产业与功能

能源、算力、农业、制造与物流的经济基础；一期岗位及技能需求。

2 · 空间结构

单一城市或多聚落选择；中心层级、组团关系、公共服务与生长方向。

3 · 交通与出行

区域连接与必要进场工程；路网、货运、公交通达、慢行及无人车与无人机。

4 · 市政与能源

取水供水回用；光伏储能配电；冷却和余热；通信、废物及保障设施。

5 · 生态与景观

季节沟道和洪水；山体与汇水保护；干旱绿化、遮阴和生产城市边缘。

6 · 城市形态与风貌

强度、高度和公共界面；高温、Zonda风、地震适应；夜间照明与暗夜。

7 · 分期实施

首批工程和服务；扩展触发、临时永久设施及难以逆转的先期决定。

关键技术问题

1 · 水资源

分项生活、冷却、农业、景观及工业用水；区分取用、回用与消耗，说明缺水时的保障顺序。

2 · 就业与人口

开城和一期建成的岗位、居民和住房；说明家庭、通勤、轮班、技能与服务人口，不能简单一人一岗。

3 · 夜间与冬季供能

说明供能、储能及备用条件，以及对设备、街道、住房和必要服务运行的影响。

4 · 人与机器

自动驾驶车辆、机器人与行人在哪里交会；分离、混行或分时如何落实到尺寸和场景。

5 · 分期触发

说明触发下一阶段的可观察条件，以及主干道路、设施和保护空间等不可逆决定。

6 · 灾害应对

山洪、地震和强风风沙的避险、停运与恢复；干河床不布置永久建筑。

分期与实施

先行区由XCITY自行建设。城市各期的位置、范围、内容与触发条件由方案论证；一期应与已有设施衔接，并具备基本生产、居住、服务和资源保障。

01

开城与一期

首批岗位、住房、公服
道路、能源、水及运营

→

02

后续扩展

人口与产业需求增长
资源和设施达到触发条件

→

03

持续调整

分阶段复核容量和风险
保留保护空间及系统弹性

各期均需提交：范围、容量、必要工程、服务对象、前置条件及扩展触发。区分计划时间与实际触发；说明后续暂缓时如何运行，以及临时设施何时转换。

后续专业深化应列明要验证的问题，不得以未来工程承诺替代本轮对空间、资源和实施关系的判断。

成果要求

第一轮：仅提交最多十页初步想法PDF（可由PPT导出），资格及团队、业绩证明另附，不计入十页上限。第一轮不要求完整规划方案，亦不支付设计补偿。

第二轮成果层次	必需表达的图纸与内容
全域战略研究	区位综合分析、空间结构、五大系统、生态水文、交通物流、资源设施和分期；含容量与依据
一期总体城市设计	总平面、用地功能、路网公交通达、公服、开放空间、市政接口、强度高度、实施计划
城市设计放大	街区地块、建筑体量和界面、服务流线、关键剖面、空间导则和同范围指标
重点节点与策略	局部总平面、建筑景观及设施关系、关键断面、使用和运行情景、代表性空间视图
技术成果	指标与依据表、资源及分期论证、假设与来源清单；采用的CAD / GIS及模型、坐标图层和查看说明
汇总与汇报	六张A0横版展板；A3文本最多60页（含附录及要求—图纸索引）；最多800词设计说明；一张预览图；主创线上汇报答疑

第二轮使用英文，展板匿名，不出现机构名或标志。附XLSX指标表与CAD/GIS文件；视频和实体模型可选，多交媒介不加分。所有图纸保持同版，标明北向、比例尺、关键尺寸及来源。

评审标准

第一轮 · 初步构想遴选

判断维度	主要证据
场地理解与初步方向	最多十页构想能识别场地资源和空间约束，提出相互联系的系统及一期判断
相关作品与实际团队	代表项目的设计质量、类似问题经验，主创及实际团队的职责、专业协作和投入
方法与可执行性	说明拟验证的问题、工作方法与资料判断，不以效果图数量或公司名气代替专业判断

第二轮 · 完整方案评审

场地解读与空间结构	场地条件实质影响选址、中心、走廊与生长
系统与资源	水、能源、算力、人口与服务相互支持
城市与空间品质	街区、公服、街道和公共空间适应不同使用者
分期与实施	一期可独立运行，工程依赖及扩展触发可信
专业接口与深化条件	各专业协调，后续需验证的问题明确
表达与沟通	图纸、数字与文字清楚且相互一致

各项权重随正式规则公布。

应征申请人的资格

Eligibility and Qualifications of Applicants

本次征集面向全球专业设计机构及联合体。以下条件用于资格审核；通过审核不等于入围五家，初步构想仍须参加统一遴选。

条件	要求与证明
合法注册	申请人应为合法注册的法人实体，或由合法注册法人组成的项目联合体；提供注册证书、营业执照或官方登记查询链接，任选一种；接受普通电子版或扫描件。
专业资格与覆盖	申请人或联合体须依法具备规划、建筑或景观设计的相关执业或经营资格，整体团队须覆盖总体规划、城市设计及景观生态能力；按注册所在地规定提供有效证明。
等效证明	所在地不实行机构资质分级的，可提交注册证明、适用的专业人员资格及业务范围说明等效材料；不统一要求中国式资质等级。
类似经验与团队	提供与本项目相关的规划设计经验、代表作品和实际职责，明确本项目主创及实际成员；说明水、能源、交通及实施等专业协作安排。
联合体与重复申请	允许联合体共同满足要求，提供协议或成员及分工说明，明确牵头方与职责；成员不得再单独申请或加入其他联合体重复申请。

专业资格用于确认身份及执业条件，作品、实际团队和最多十页初步构想共同用于择优遴选。所提交材料须真实、可核实，并披露与主办方、评审人员的利益关系。

在线注册与专属申请

在线申请：xcityus.github.io/xcity-ai-competition/practice.html#apply

01 在线注册

现已开放申请。在官网机构征集页填写机构、国家或地区、联系人与邮箱即可，首次注册无需附件。

02 接收专属链接

我们将通过邮件发送专属申请链接。在官网专属页逐项填写资格表并提供材料；Word工作表仅供可选准备。

03 在线填写与保存

通过专属页填写资格表，上传适用证明、团队业绩或接受的链接，以及1–10页构想PDF。可保存进度后继续；无需上传Word，邮件不收申请附件。

04 进入第一阶段审核

2026年12月31日23:59 UTC截止注册；2027年1月31日23:59 UTC前在官网最终提交完整申请；2027年2月遴选五家。仅注册或保存草稿不代表完成第一阶段申请或入围。

证明支持普通PDF、PNG、JPG或接受的链接，不要求公证；单个文件最多10 MB，合计最多25 MB；构想为1–10页PDF。联系：competition@xcity.ai。

第一轮 · 最多十页初步想法

用最多十页说明你们如何判断场地、组织城市，以及入围后将验证什么。此阶段重在设计方向和工作方法，不要求提前完成整套规划。下列五项为建议内容，各项页数可自行分配。

建议内容	应说明的内容
1 场地判断与核心问题	识别地形、水、气候、资源与区域联系中真正影响规划的条件，提出优先解决的问题。
2 全域与五大系统	用简明示意说明能源算力、农业、居住公共生活、产业自动化及对外物流如何共同组织场地。
3 一期启动逻辑	提出初步启动位置或选址原则，解释生产、住房、公共服务和必要基础设施如何相互支持。
4 代表性空间想法	用草图、关系图或剖面展示一个有代表性的空间判断，说明它如何验证总体思路；不要求精细效果图。
5 方法与专业协作	说明入围后的研究路径、关键假设、需要验证的问题及专业协作安排。

格式与工作量

提交最多十页PDF，可由PPT导出。资格、团队及业绩证明另附，不计入十页上限。无需另交完整总平面、工程测算或额外效果图。

遴选与成果使用

专家按第13章标准，结合构想、作品和实际团队选出5家。第一轮不付费；未入围构想不授予主办方改编或实施权。

第二轮完整设计、补偿与优胜奖金

5家入围机构签订参赛协议并收到完整任务书及统一资料包后，开展第二轮设计。第一轮获选即取得参与有偿设计的资格，不代表入围时即支付补偿。

项目	名额与金额	付款条件
第二轮设计补偿	5家 × US$50,000 合计 US$250,000	按任务书及参赛协议完整提交有效第二轮成果后支付；不以是否获奖为条件
优胜额外奖金	1家 × US$50,000	评审结果公布后，向优胜机构另行支付；叠加其设计补偿
总额	US$300,000	优胜机构合计US$100,000；其余4家各US$50,000

有效提交的含义

按统一规定提交本轮必需成果，对设计任务作出实质回应。机构资格在前期审核；成果完整性检查与设计质量评审分别进行，排名靠后不取消补偿。

费用边界

第一轮不付费，第二轮无启动预付款。不设另行深化奖金；后续设计不包含在本轮补偿或优胜奖金内。税务、付款凭证及结算手续按签订的参赛协议执行。

线上组织、专家评审与成果使用

线上组织与资料

不组织现场踏勘。主办方提供统一场地资料包，开展线上场地介绍与协调答疑；影响设计的补充资料和答复统一提供给相应阶段的所有参与机构。

专家评审

由具备相关专业能力的专家组成评审团，按公布标准评选。评委应披露利益冲突并回避；评审团详情确定后，由主办方通过统一联系渠道通知。

Publicity + Terms · 署名、展示与后续工作

机构保留成果著作权，并保证原创及第三方材料授权。第二轮机构向主办方授予竞赛评审、展览、出版和宣传所需的非独占使用许可，主办方使用时保留署名；使用范围不自动包括修改、实施或项目之外的商业用途。第一轮构想仅用于遴选，公开展示另征得作者同意。

主办方可邀请优胜团队洽谈后续深化委托。具体服务范围、费用及修改和实施所需权利另行签约；获奖不自动构成后续委托合同，补偿及奖金不抵扣另行约定的深化设计费。

场地资料

资料	使用说明
场地边界与先行区	统一版本的空间文件及精度说明；竞赛范围约1,656 km²；固定试点含光伏农业田13.9 km²、生活区一期2.48 km²
区位与真实影像	区域关系、卫星影像及现状道路；影像标明来源，区别多期拼接与现场测量
地形与水文筛查	高程坡度、季节性沟道、洪泛敏感性及初步适建筛查；保留方法和适用边界
系统意向与设施参考	五大系统意向、农光共生及POD图像；参考意向不能作为固定选址或性能证明
版本、假设与公开范围	所有成果注明资料版本与来源；精度不足和未落实资源条件列入假设及影响说明

资料包、答疑与补遗采用统一发布渠道。后续勘察、地籍、水权及专项核实不由示意地图替代；资料缺口本身不作为申请者或方案的扣分理由。

联系方式

XCITY

机构赛道 · 国际总体规划与城市设计竞赛

现已开放在线注册。我们将邮件发送专属申请链接；请在官网逐项填写资格表、上传或提供接受的链接，可保存并最终提交。邮件不收申请附件。所有申请人适用统一申请要求、资格审核与评审标准。资料、澄清及通知通过官方渠道统一发布；问题可联系下列邮箱。

在线申请：xcityus.github.io/xcity-ai-competition/practice.html#apply

联系邮箱： competition@xcity.ai